


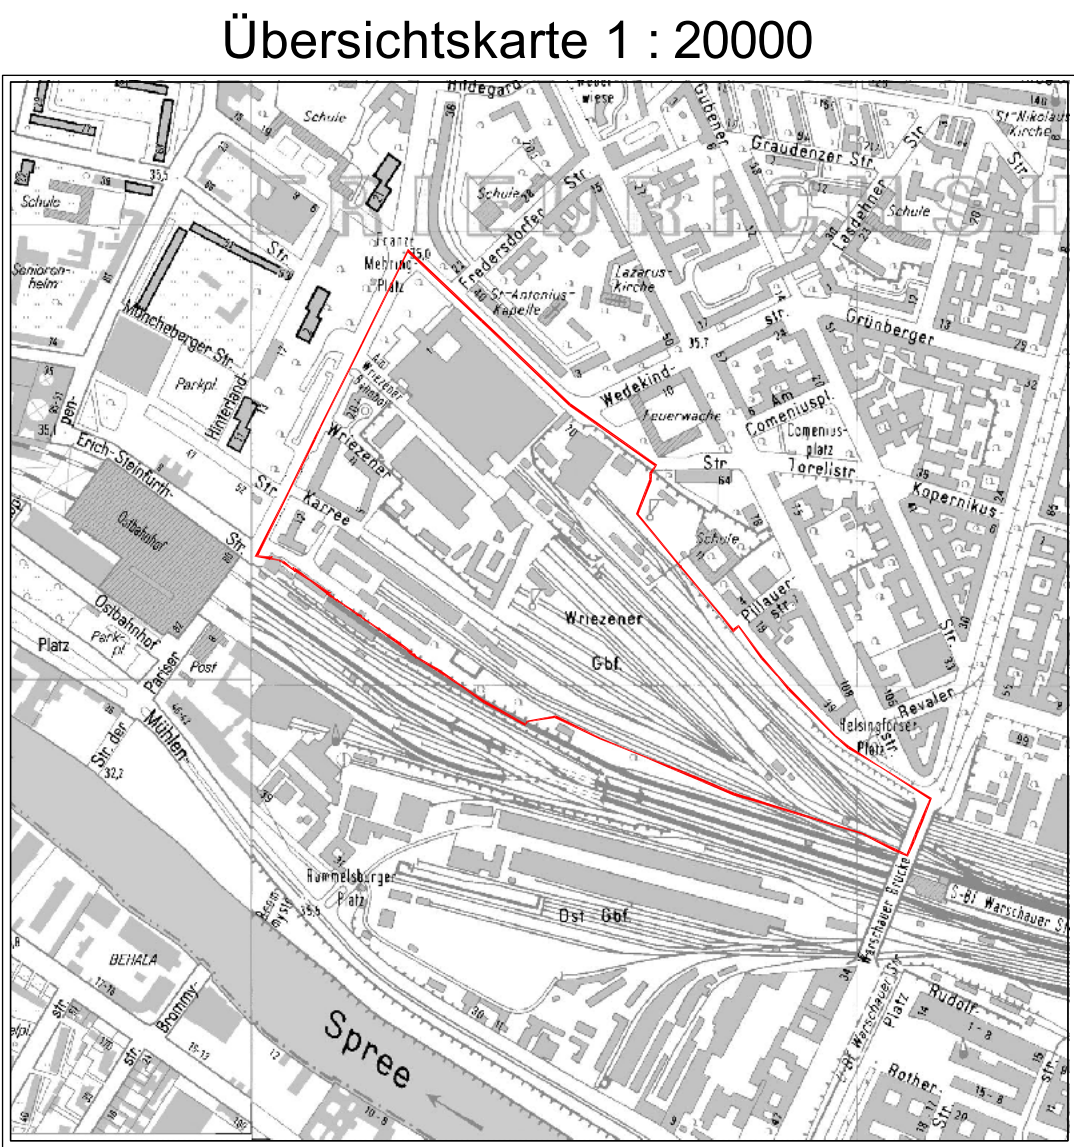

Textliche Festsetzungen

- Im eingeschränkten Gewerbegebiet sind nur Betriebe und Anlagen zulässig, die das Wohnen nicht wesentlich stören.
- Im Gewerbegebiet GE4 ist großflächiger Einzelhandel mit einer Verkaufsfläche bis zu 2.600m² zulässig.
- Das Sondergebiet SO1 dient überwiegend der Ansiedlung eines großflächigen Einzelhandelsbetriebes mit der Zweckbestimmung Bau- und Heimwerkermarkt mit Gartencenter. Zulässig ist ein Bau- und Heimwerkermarkt mit Gartencenter einschließlich der zu diesem gehörenden Büro und Sozialräume bis zu einer Geschossfläche von 13.000 m². Dabei dürfen die nachfolgend aufgeführten Einzelhandelsortimente insgesamt 1.200m² Geschossfläche nicht überschreiten:
 - Textilien
 - Bekleidung
 - Schuhe und Lederwaren
 - Beleuchtungsartikel
 - Haushaltsgegenstände aus Metall und Kunststoff
 - Keramische Erzeugnisse und Glaswaren
 - Heimtextilien und Teppiche
 - Kork- und Korbwaren
 - Elektrische Haushaltsgeräte
- Bauliche Anlagen dürfen in den Baugebieten GE1, GE3, GE4, GE5 und SO1 eine Höhe von 51m ü. NHN und im Baugebiet GE2 eine Höhe von 46m ü. NHN nicht überschreiten. Dies gilt nicht für technische Aufbauten wie Schornsteine und Lüftungsanlagen.
- An die Baulinien in den Mischgebieten MI1, MI2 und MI3 darf bezogen auf die generell zulässige Zahl der Vollgeschosse mit Einschränkung der Tiefe der Abstandsflächen nach der Bauordnung für Berlin hergebaut werden.
- Im SO1 darf bezogen auf die generell zulässige Höhe der baulichen Anlagen an die Grenze zum GE3 mit Einschränkung der Tiefe der Abstandsflächen nach der Bauordnung für Berlin hergebaut werden. Die einzuhaltenden Abstandsflächen betragen 0,25H, mindestens 3m.
- Innerhalb der Fläche ABCDA ist eine Werbeanlage (Pylon) mit einer Höhe bis zu 61m über NHN zulässig.
- Überdachte Stellplätze sind auf den nicht überbaubaren Grundstücksflächen nur innerhalb der Fläche EFGHE zulässig.
- Die Einteilung der Straßenverkehrsfläche ist nicht Gegenstand der Festsetzung.
- Im Geltungsbereich des Bebauungsplans ist die Verwendung von Erdgas oder Heizöl EL als Brennstoff zugelassen. Die Verwendung anderer Brennstoffe ist dann zulässig, wenn sichergestellt ist, dass die Emissionswerte von Schwefeldioxid (SOx), Stickstoffdioxid (NOx) und Staub in Kilogramm Schadstoff pro Tera Joule Energiegehalt (kg/TJ) des eingesetzten Brennstoffs vergleichbar höchstens denen von Heizöl EL entsprechen.
- Auf den Flächen zum Anpflanzen P1 und P2 ist jeweils eine Baumreihe anzulegen, zu pflegen und bei Abgang zu ersetzen. Zulässig sind schlanke, hochkronige Arten, gepflanzt in einem Abstand von höchstens 7m.
- Ebenerdige Stellplätze sind durch Flächen, die zu bepflanzen sind, zu gliedern. Je vier Stellplätze ist ein Baum zu pflanzen.
- Dachflächen mit einer Neigung von weniger als 15° sind extensiv zu begrünen; dies gilt nicht für technische Einrichtungen, für Beleuchtungsflächen und Terrassen.
- In den Baugebieten GE1, GE2 und SO1 sind für die anfallenden Niederschlagswasser Versickerungsflächen anzulegen und das Niederschlagswasser ist zu versickern, sofern wasserwirtschaftliche Belange dem nicht entgegenstehen. Die Versickerungsflächen sind zu begrünen. Ausnahmsweise können andere technische Einrichtungen zugelassen werden.
- Fensterlose Außenwandflächen von Gebäuden ab einer Größe von 100m² sowie Außenwandflächen von Nebenanlagen gemäß § 14 (1) BauNVO sind mit rankenden, schlingenden oder selbstklimmenden Pflanzen zu begrünen.
- Ebenerdige Stellplatzanlagen an öffentlichen Verkehrsflächen sind durch Einfriedungen abzugrenzen. Zulässig sind die Kombination aus Mauern mit einer Höhe von mindestens 0,5m bis maximal zu einer Höhe von 0,6m und einer dahinter angrenzenden Hecke mit einer Höhe bis zu 1,20m oder nur eine Hecke bis zu einer Höhe von 1,20m.

2 - 11

Maßstab 1 : 2 000



Planunterlage: Flurkarte, automatische Liegenschaftskarte und Ergänzungsmessungen
Stand: August 2004

- Die Flächen G1 und G4 sind mit einem Geh- und Fahrrecht zugunsten der Benutzer und Besucher des Sondergebietes SO 2 Kultur und Vergnügungsstätte zu belasten.
- Die Fläche G2 ist mit einem Geh- und Fahrrecht für den Träger der Straßenbaulast zugunsten der Allgemeinheit und mit einem Leitungsrecht zugunsten der zuständigen Unternehmensträger zu belasten.
- Die Flächen G3 und G4 sind mit einem Gehrecht zugunsten der Allgemeinheit zu belasten. Mit Entwidmung der angrenzenden Bahnanlage und Einbeziehung in die öffentliche Parkanlage kann das Gehrecht G3 entfallen.
- Die nachrichtlich übernommene Bahnfläche im Geltungsbereich des Bebauungsplans ist nur bis zu ihrer Entwidmung zulässig. Nach Eintritt der Entwidmung der Fläche wird die Fläche als öffentliche Grünfläche mit der Zweckbestimmung öffentliche Parkanlage festgesetzt.



Nebenzonierung 1
Festsetzung nach Entwidmung der Bahnflächen

Stand des Bebauungsplans:
Festsetzungsbeschluss des Bezirkes
vom 14. Dezember 2005

Der vorliegende Plan ist eine Umzeichnung des Originals.
Das Original ist im Maßstab 1 : 1000 und in 2 Blätter geteilt.

Bebauungsplan 2 - 11

für das Gebiet zwischen
Rüdersdorfer Straße, Helsingförscher Straße,
Warschauer Straße, Bahnanlagen und
Straße der Pariser Kommune

im Bezirk Friedrichshain-Kreuzberg,
Ortsteil Friedrichshain

Zeichenerklärung Festsetzungen

Art und Maß der baulichen Nutzung, Bauweise, Baulinien, Baugrenzen, Höhe baulicher Anlagen

Mischgebiet	(§ 6 BauNVO)	MI	Zahl der Vollgeschosse als Höchstmaß	z.B.	III
Gewerbegebiet	(§ 8 BauNVO)	GE	als Mindest- und Höchstmaß	z.B.	III-V
Gewerbegebiet eingeschränkt	(§ 8 BauNVO)	GEe			
Sondergebiet	(§ 11 BauNVO)	SO			

Geschossflächenzahl	als Höchstmaß z.B.	0,7	Baulinie	(§ 23 Abs.2 Satz.1 BauNVO)	
Grundflächenzahl	als Höchstmaß z.B.	0,4	Baugrenze	(§ 23 Abs.3 Satz.1 BauNVO)	
Baumassenzahl	als Höchstmaß z.B.	3,0			

Höhe baulicher Anlagen über einem Bezugspunkt
als Höchstmaß

Oberkante z.B. **OK** 55 m über NHN

Verkehrsflächen			
Straßenverkehrsflächen		Straßenbegrenzungslinie	
Flächen für Versorgungsanlagen			
Öffentliche und Private Grünflächen			

z.B. **ÖFFENTLICHE PARKANLAGE**
z.B. **PRIVATE DAUERKLEINGÄRTEN**

Anpflanzungen, Bindungen für Bepflanzungen, Schutz und Entwicklung von Boden,
Natur und Landschaft

Umgrenzungen von Flächen zum Anpflanzen		Erhaltung von Bäumen	
--	--	----------------------	--

Sonstige Festsetzungen

Mit Geh-, Fahr- u. Leitungsrechten zu
belastende Flächen

Grenze des räumlichen Geltungsbereiches
des Bebauungsplanes

Abgrenzung unterschiedlicher Nutzung			
--------------------------------------	--	--	--

Nachrichtliche Übernahmen

Einzelanlage, die dem Denkmalschutz unterliegt		Bahnanlagen	
Gesamtanlage (Ensemble), die dem Denkmalschutz unterliegt		Fläche über Leitungsbestand	

Eintragungen als Vorschlag

Brücke			
Planunterlage			
Öffentliches oder Wohngebäude mit Geschosszahl und Durchst.		Grenze von Berlin	
Wirtschafts-, Industriegebäude oder Garage		Bezirksgrenze	
Parkhaus		Ortssteilgrenze	
unterirdisches Bauwerk mit Geschosszahl		Gemarkungsgrenze	
Brücke		Flurgrenze	
Gewässer		Flurstücksgrenze	
Geländehöhe, Straßenhöhe in m über NHN		Flurstücksnummer, Flurnummer	
Laubbaum, Nadelbaum		Grundstücksnummer	
Naturdenkmal (Laub-, Nadelbaum)		Mauer	
Schornstein		Stützmauer	
Zaun, Hecke		Bordkante	
Hochspannungsmast		Baulinie, Baugrenze	
Straßenbegrenzungslinie			

Die vorstehende Zeichenerklärung enthält gebräuchliche Planzeichen, auch soweit sie in diesem
Bebauungsplan nicht verwendet werden. Zugrunde gelegt sind die Baunutzungsverordnung (BauNVO) in
der Fassung vom 23. Januar 1990 und die Planzeichenverordnung 1990 (PlanzV90)
vom 18. Dezember 1990.

Aufgestellt: Berlin, den

Bezirksamt Friedrichshain - Kreuzberg von Berlin
Abt. Stadtentwicklung und Bauen

Amt für Stadtplanung und Vermessung
Fachbereich Vermessung

Bezirksstadtrat

Amt für Stadtplanung und Vermessung
Fachbereich Stadtplanung

Der Bebauungsplan wurde in der Zeit vom
Die Bezirksverordnetenversammlung hat den Bebauungsplan am

bis einschließlich
öffentlich ausgelegt,
beschlissen.

Berlin, den

Bezirksamt Friedrichshain - Kreuzberg von Berlin
Abt. Stadtentwicklung und Bauen
Amt für Stadtplanung und Vermessung
Fachbereich Stadtplanung

Fachbereichsleiter Stadtplanung

Der Bebauungsplan ist auf Grund des § 10 Abs.1 des Baugesetzbuchs in Verbindung mit § 6 Abs. 5
des Gesetzes zur Ausführung des Baugesetzbuchs durch Verordnung vom heutigen Tage festgesetzt worden.

Berlin, den
Bezirksamt Friedrichshain - Kreuzberg von Berlin

Bezirksbürgermeister

Bezirksstadtrat

Die Verordnung ist am

im Gesetz- und Verordnungsblatt Berlin auf Seite

veröffentlicht worden.

Zu diesem Bebauungsplan gehört ein Grundstücksverzeichnis